


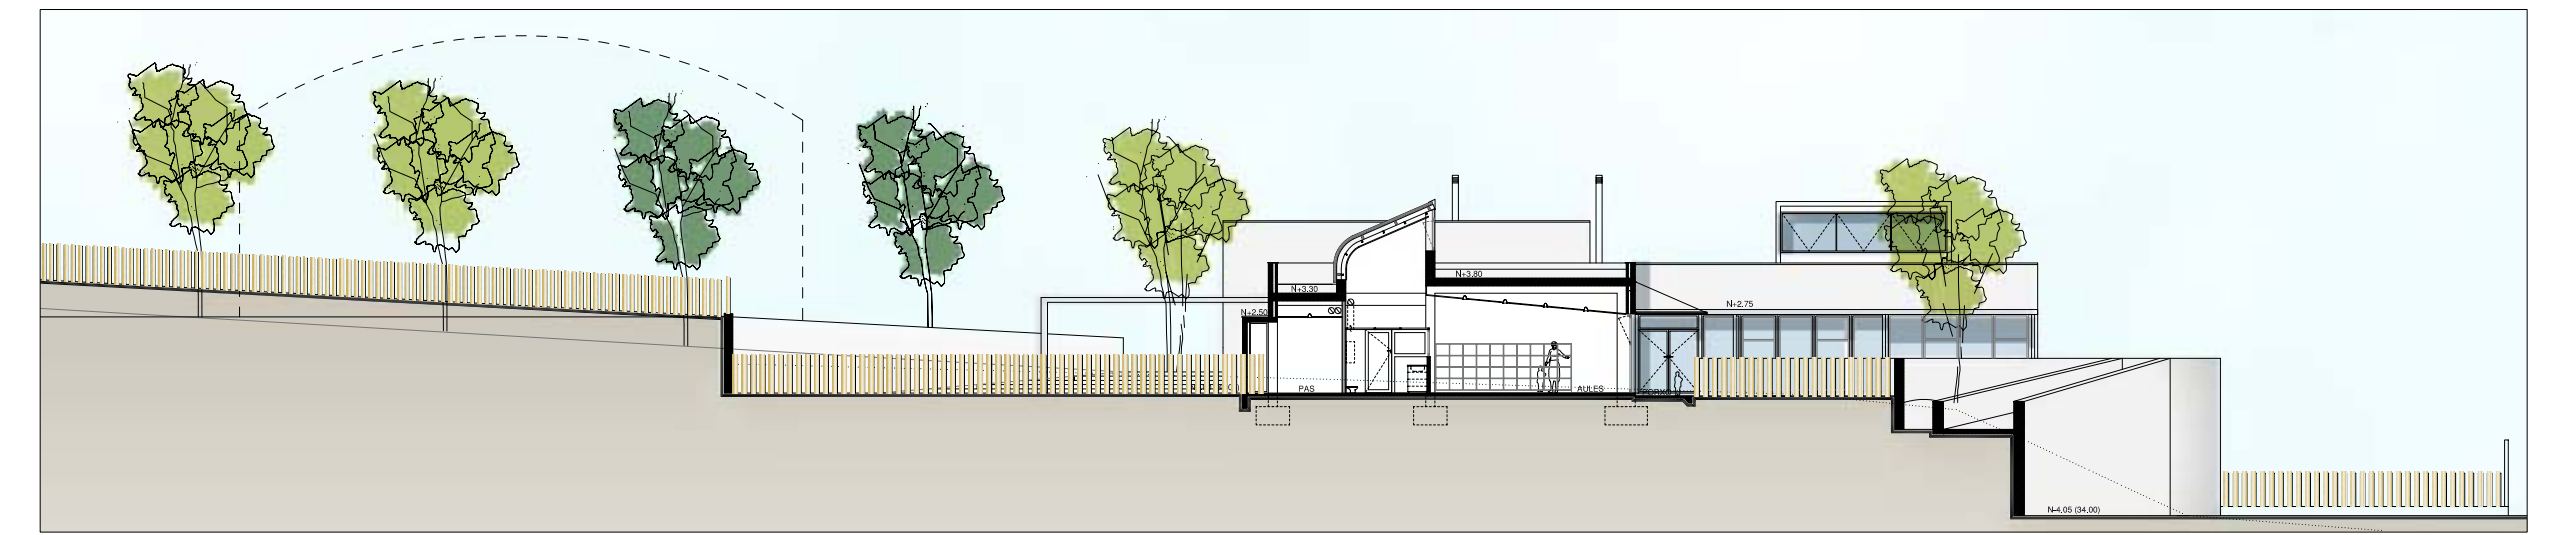


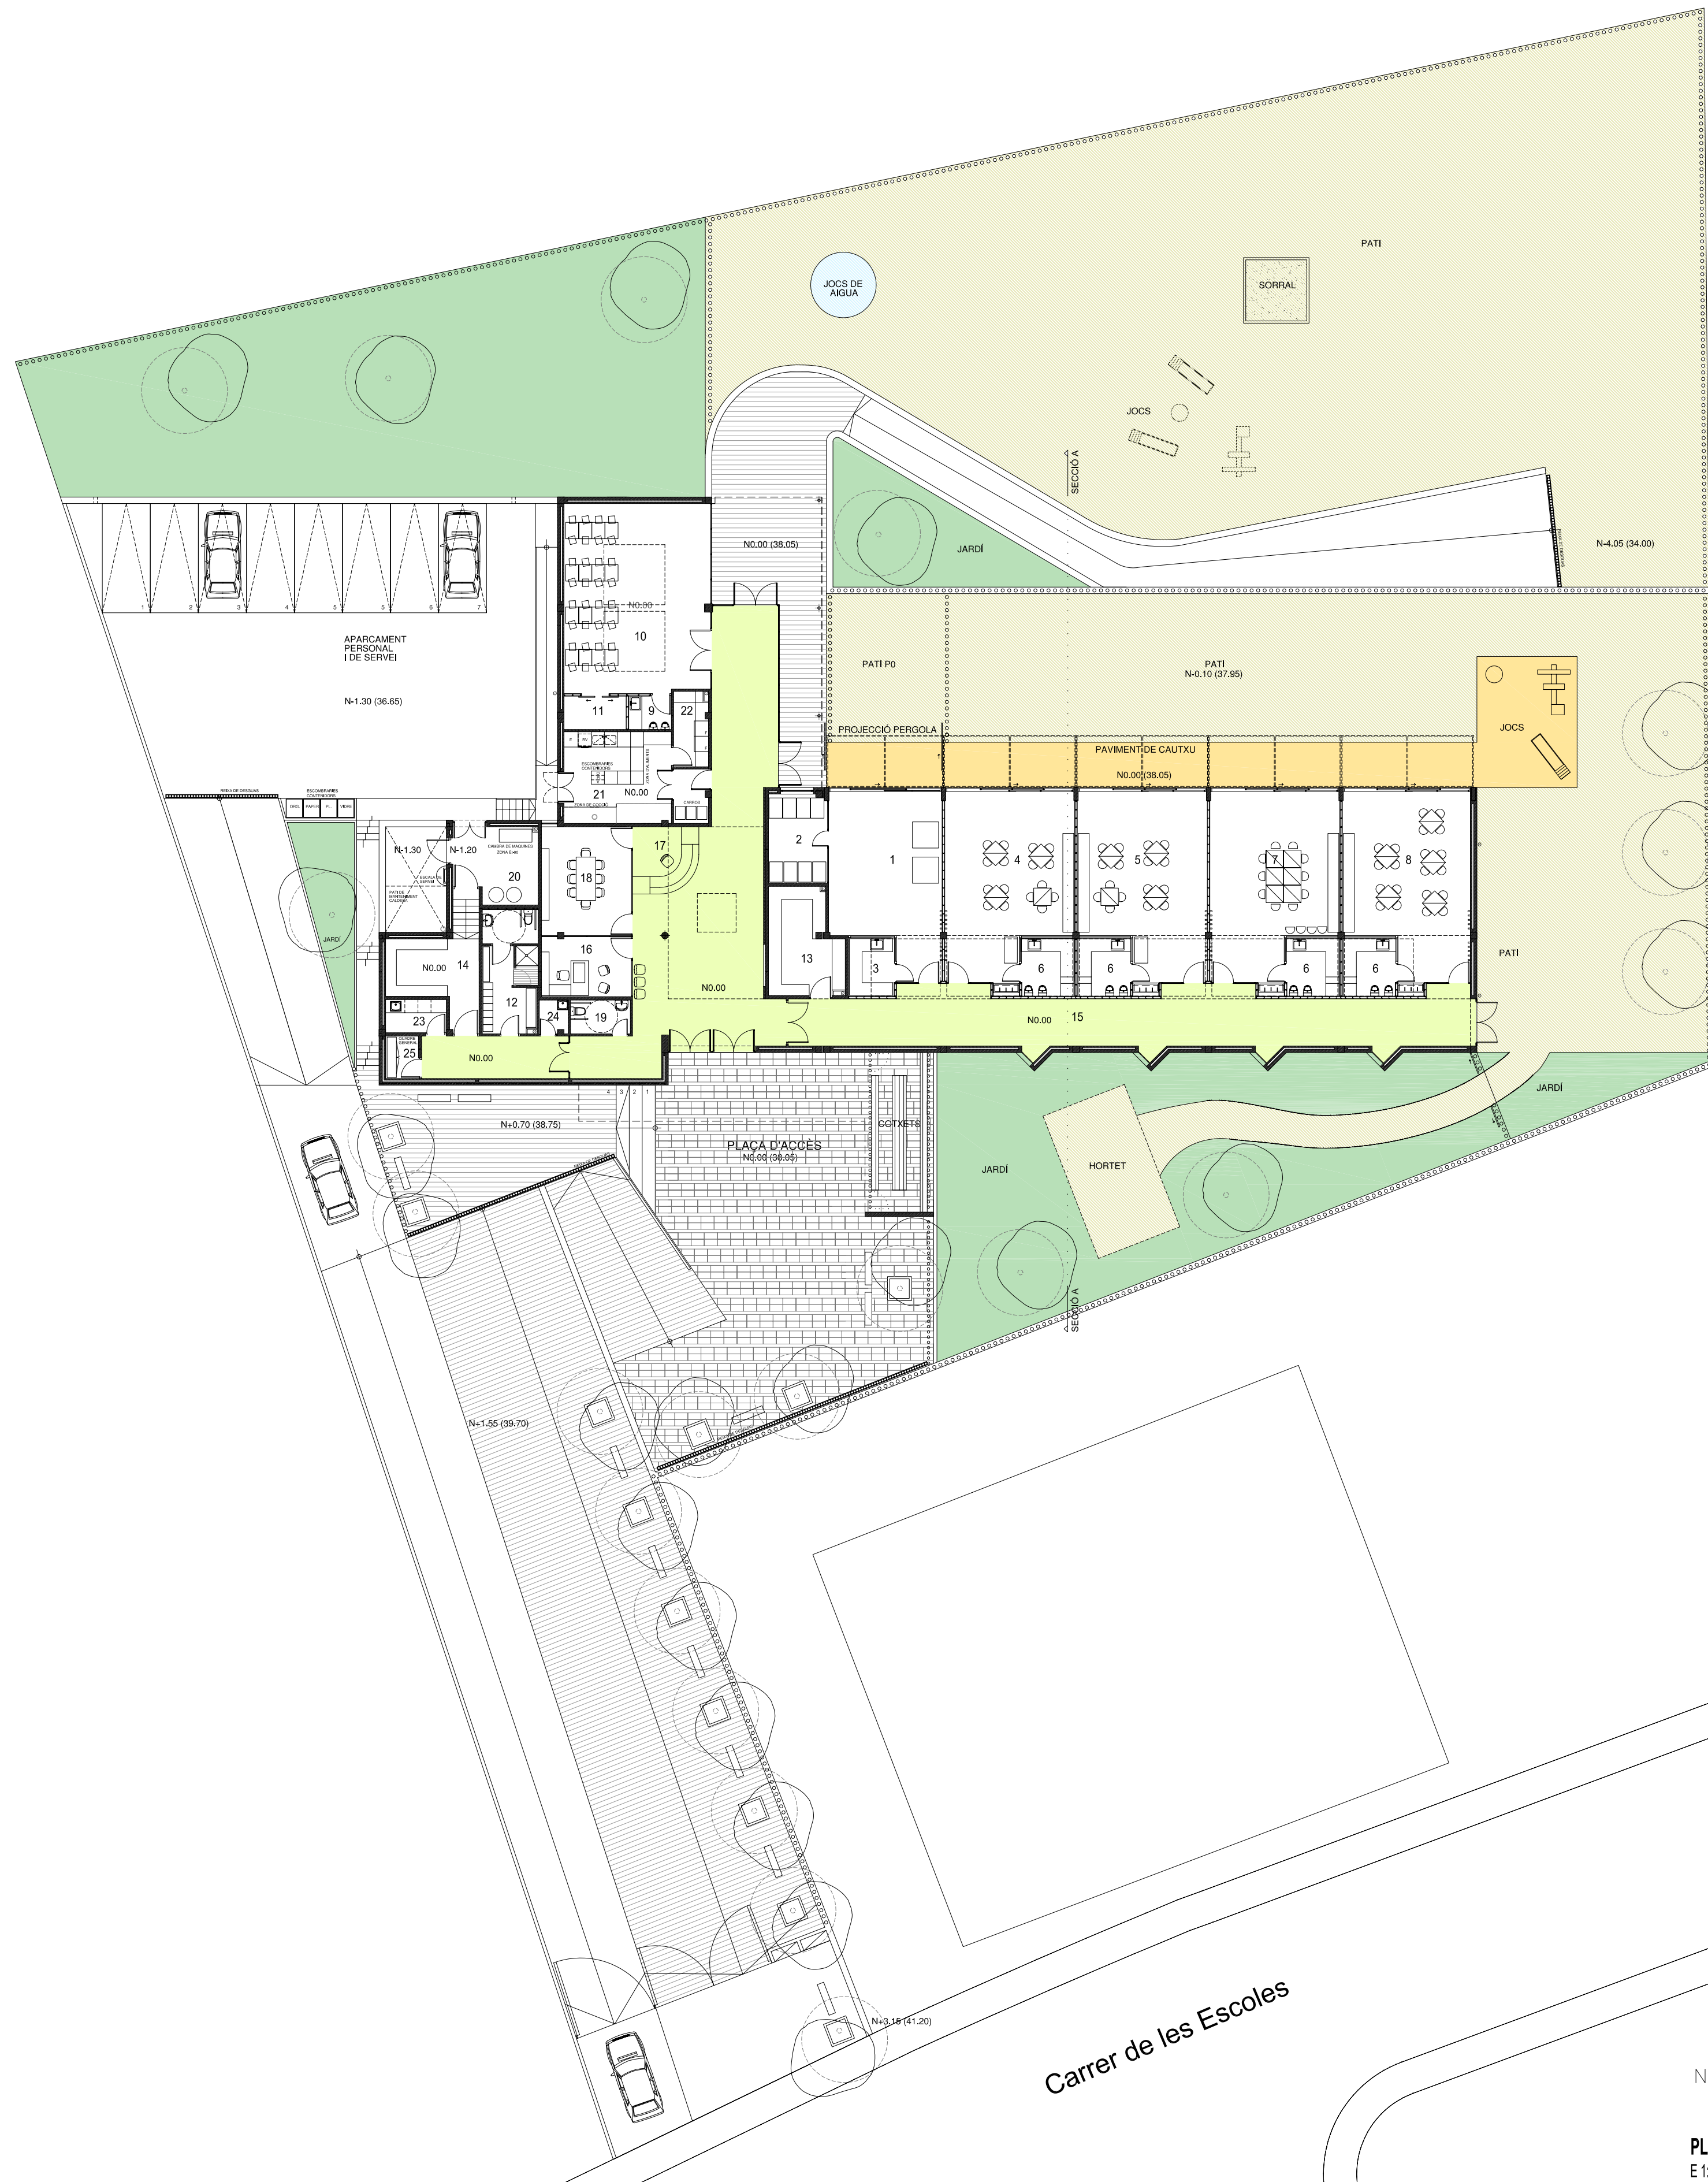

SECCIÓ
E 1:250

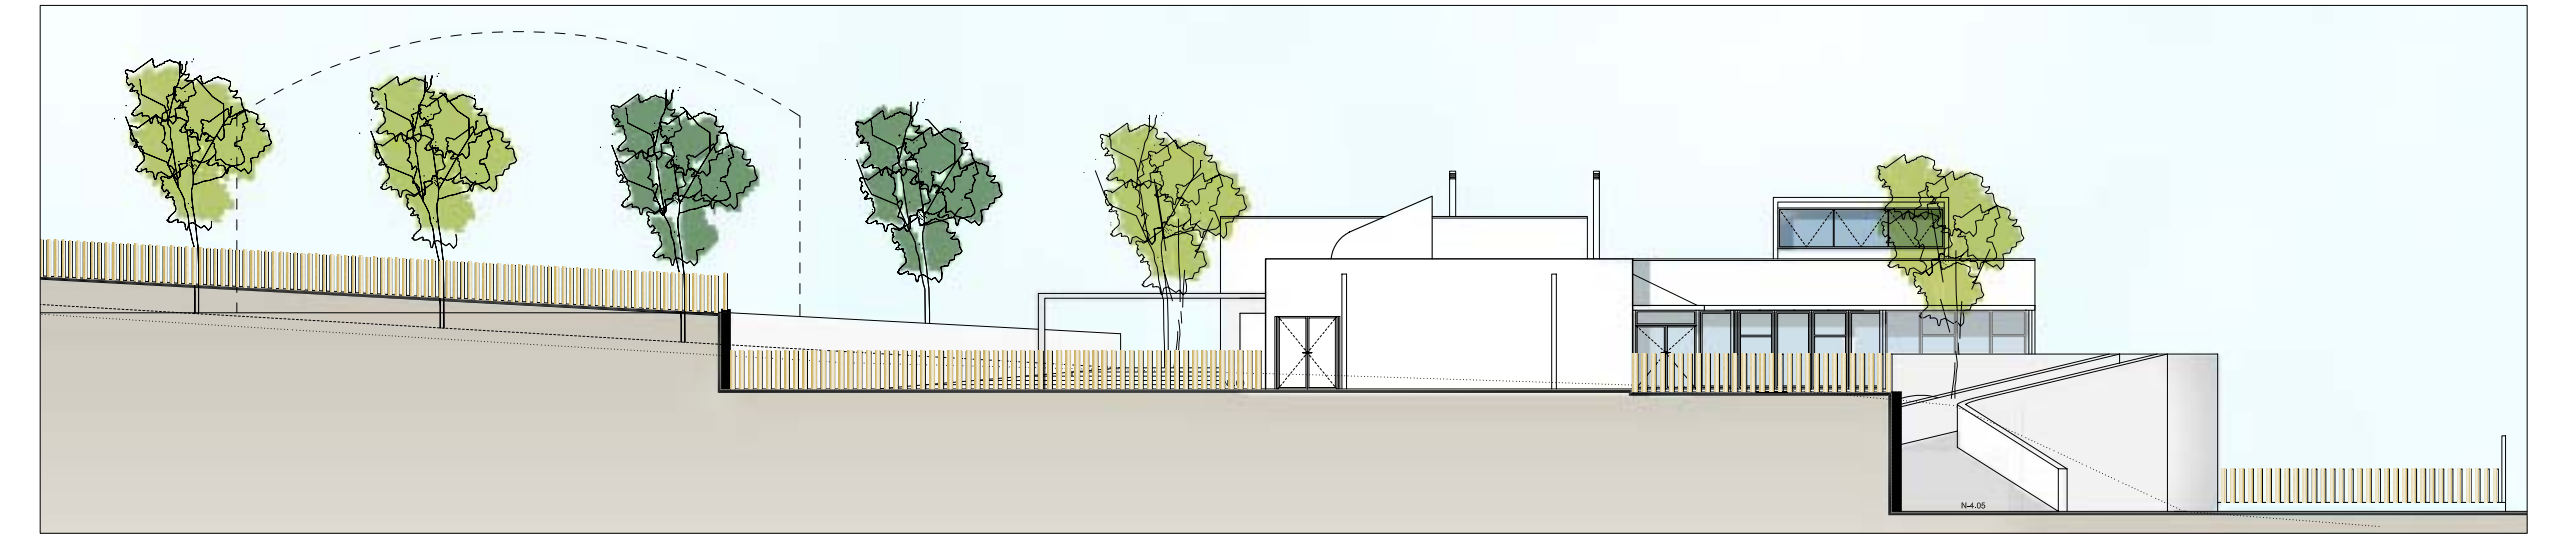

ALÇAT SUD
E 1:250

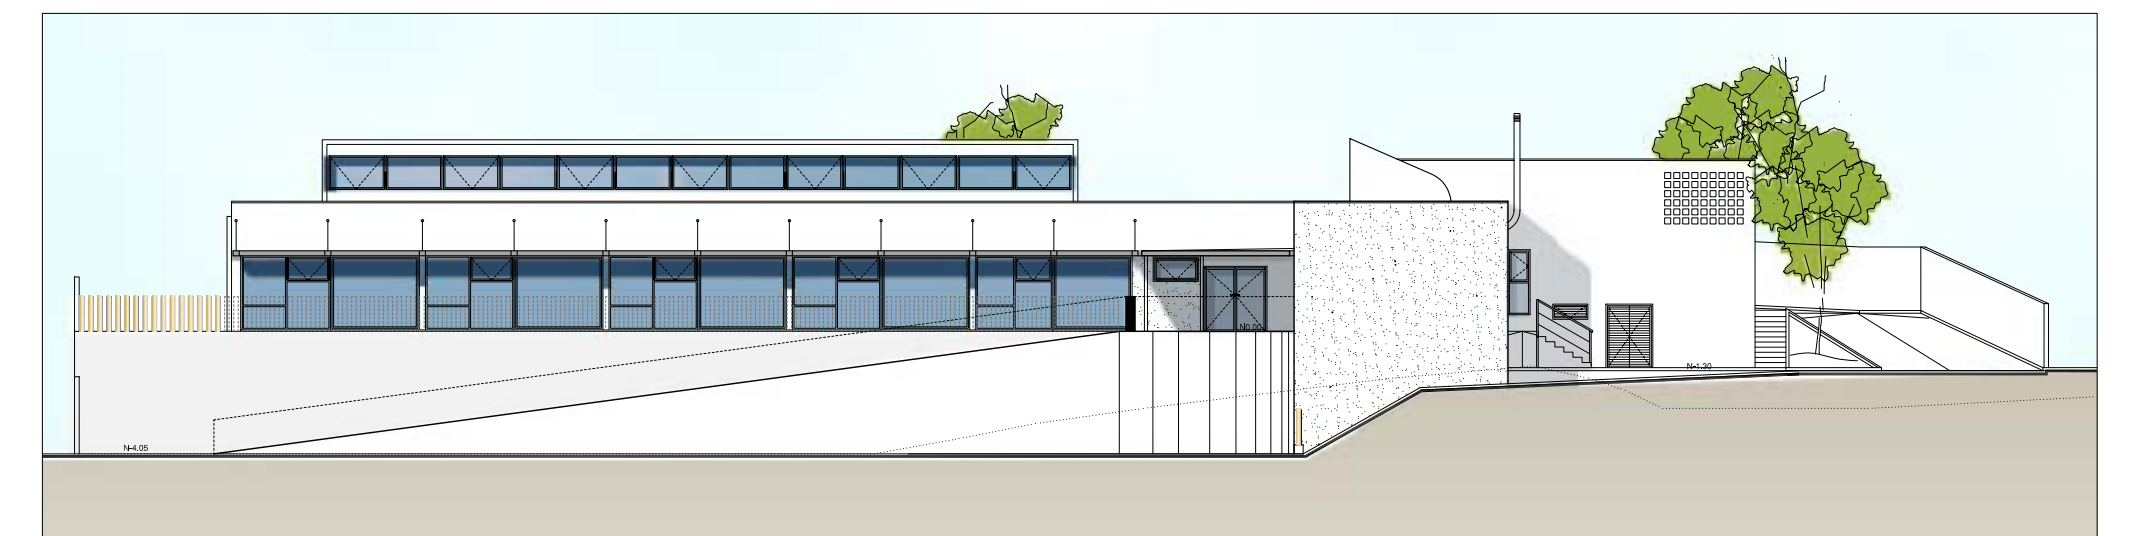


ALÇAT EST
E 1:250



ALÇAT OEST
E 1:250

PROGRAMA FUNCIONAL
LLAR D'INFANTS 72 NENS

ESPAIS		superfície (m2)			
			13	MAGATZEM MATERIAL AULES	15,25
			14	MAGATZEM GENERAL	13,75
1	AULA P0 (8 NENS)	38,80	15	PAS	186,65
2	DORMITORI P0	10,90	16	DESPATX VISITES	11,30
3	SALA CANVIADOR P0	6,00	17	SECRETARIA RECEPCIÓ	8,65
4	AULA P1-1 (14 NENS)	47,30	18	SALA PERSONAL	20,50
5	AULA P1-2 (14 NENS)	47,30	19	W.C	4,25
6	LAVABO CANVIADOR (x2)	26,00	20	SALA TÈCNICA/MAQUINARIA	13,20
7	AULA P2-1 (18 NENS)	47,30	21	CUINA	24,65
8	AULA P2-2 (18 NENS)	46,50	22	REBOST	5,50
9	W.C/SALA POLIVALENT	3,00	23	BUGADERIA	4,05
10	MENJADOR/SALA POLIVALENT	58,00	24	NETEJA	2,00
11	MAGATZEM SALA POLIVALENT	4,35	25	QUADRE GENERAL	2,90
				TOTAL SUPERFÍCIE ÚTIL	662,60
				TOTAL SUPERFÍCIE CONST.	775,15
				ZONES EXTERIORS	2.945,90

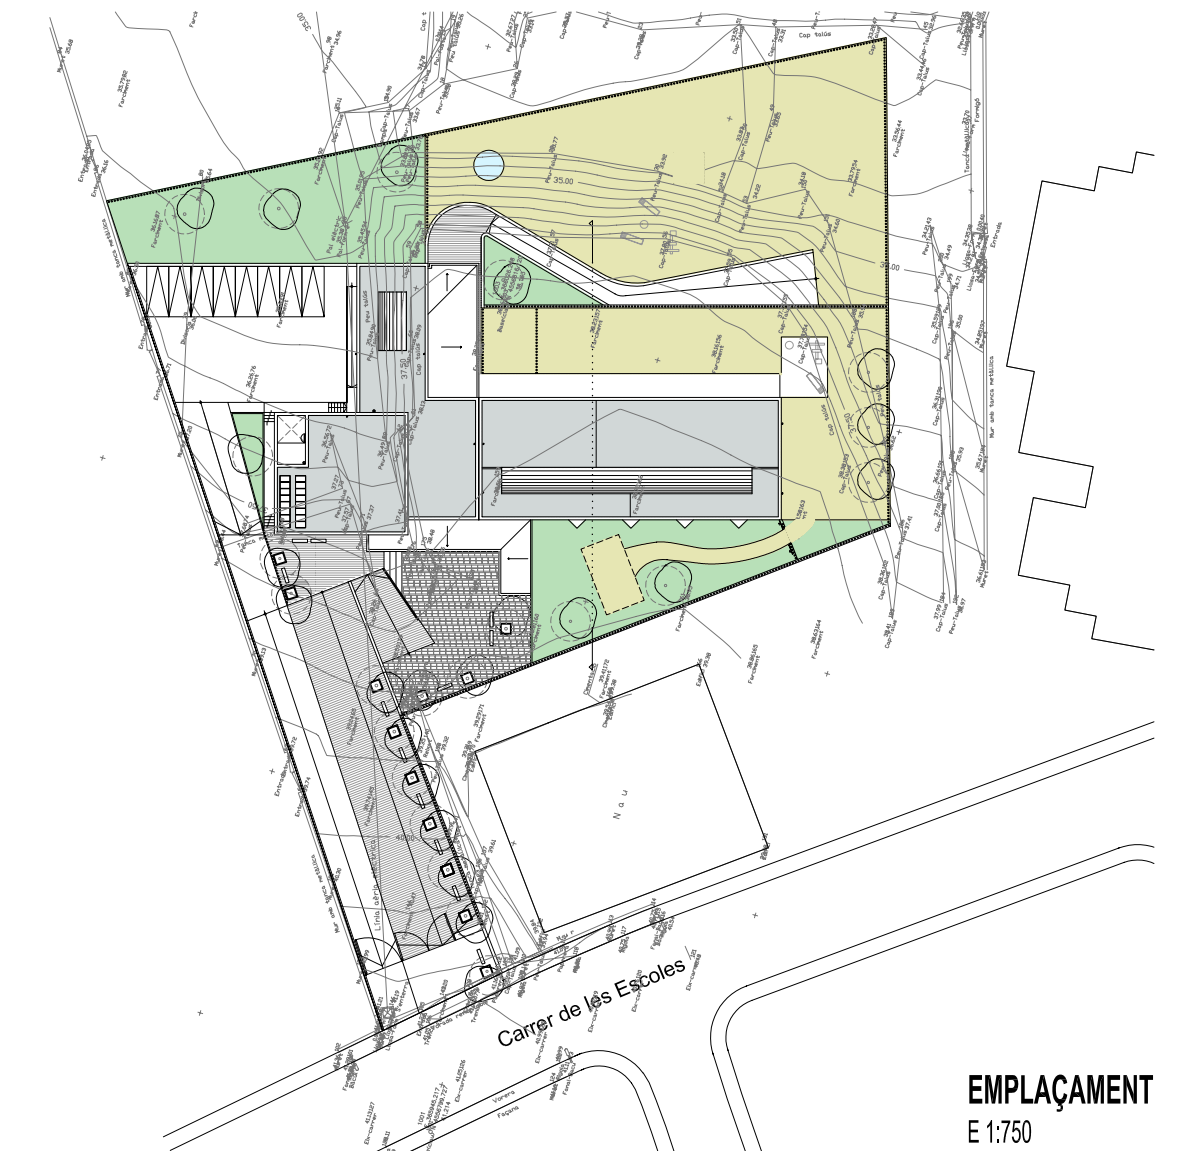

EMPLAÇAMENT
E 1:750